



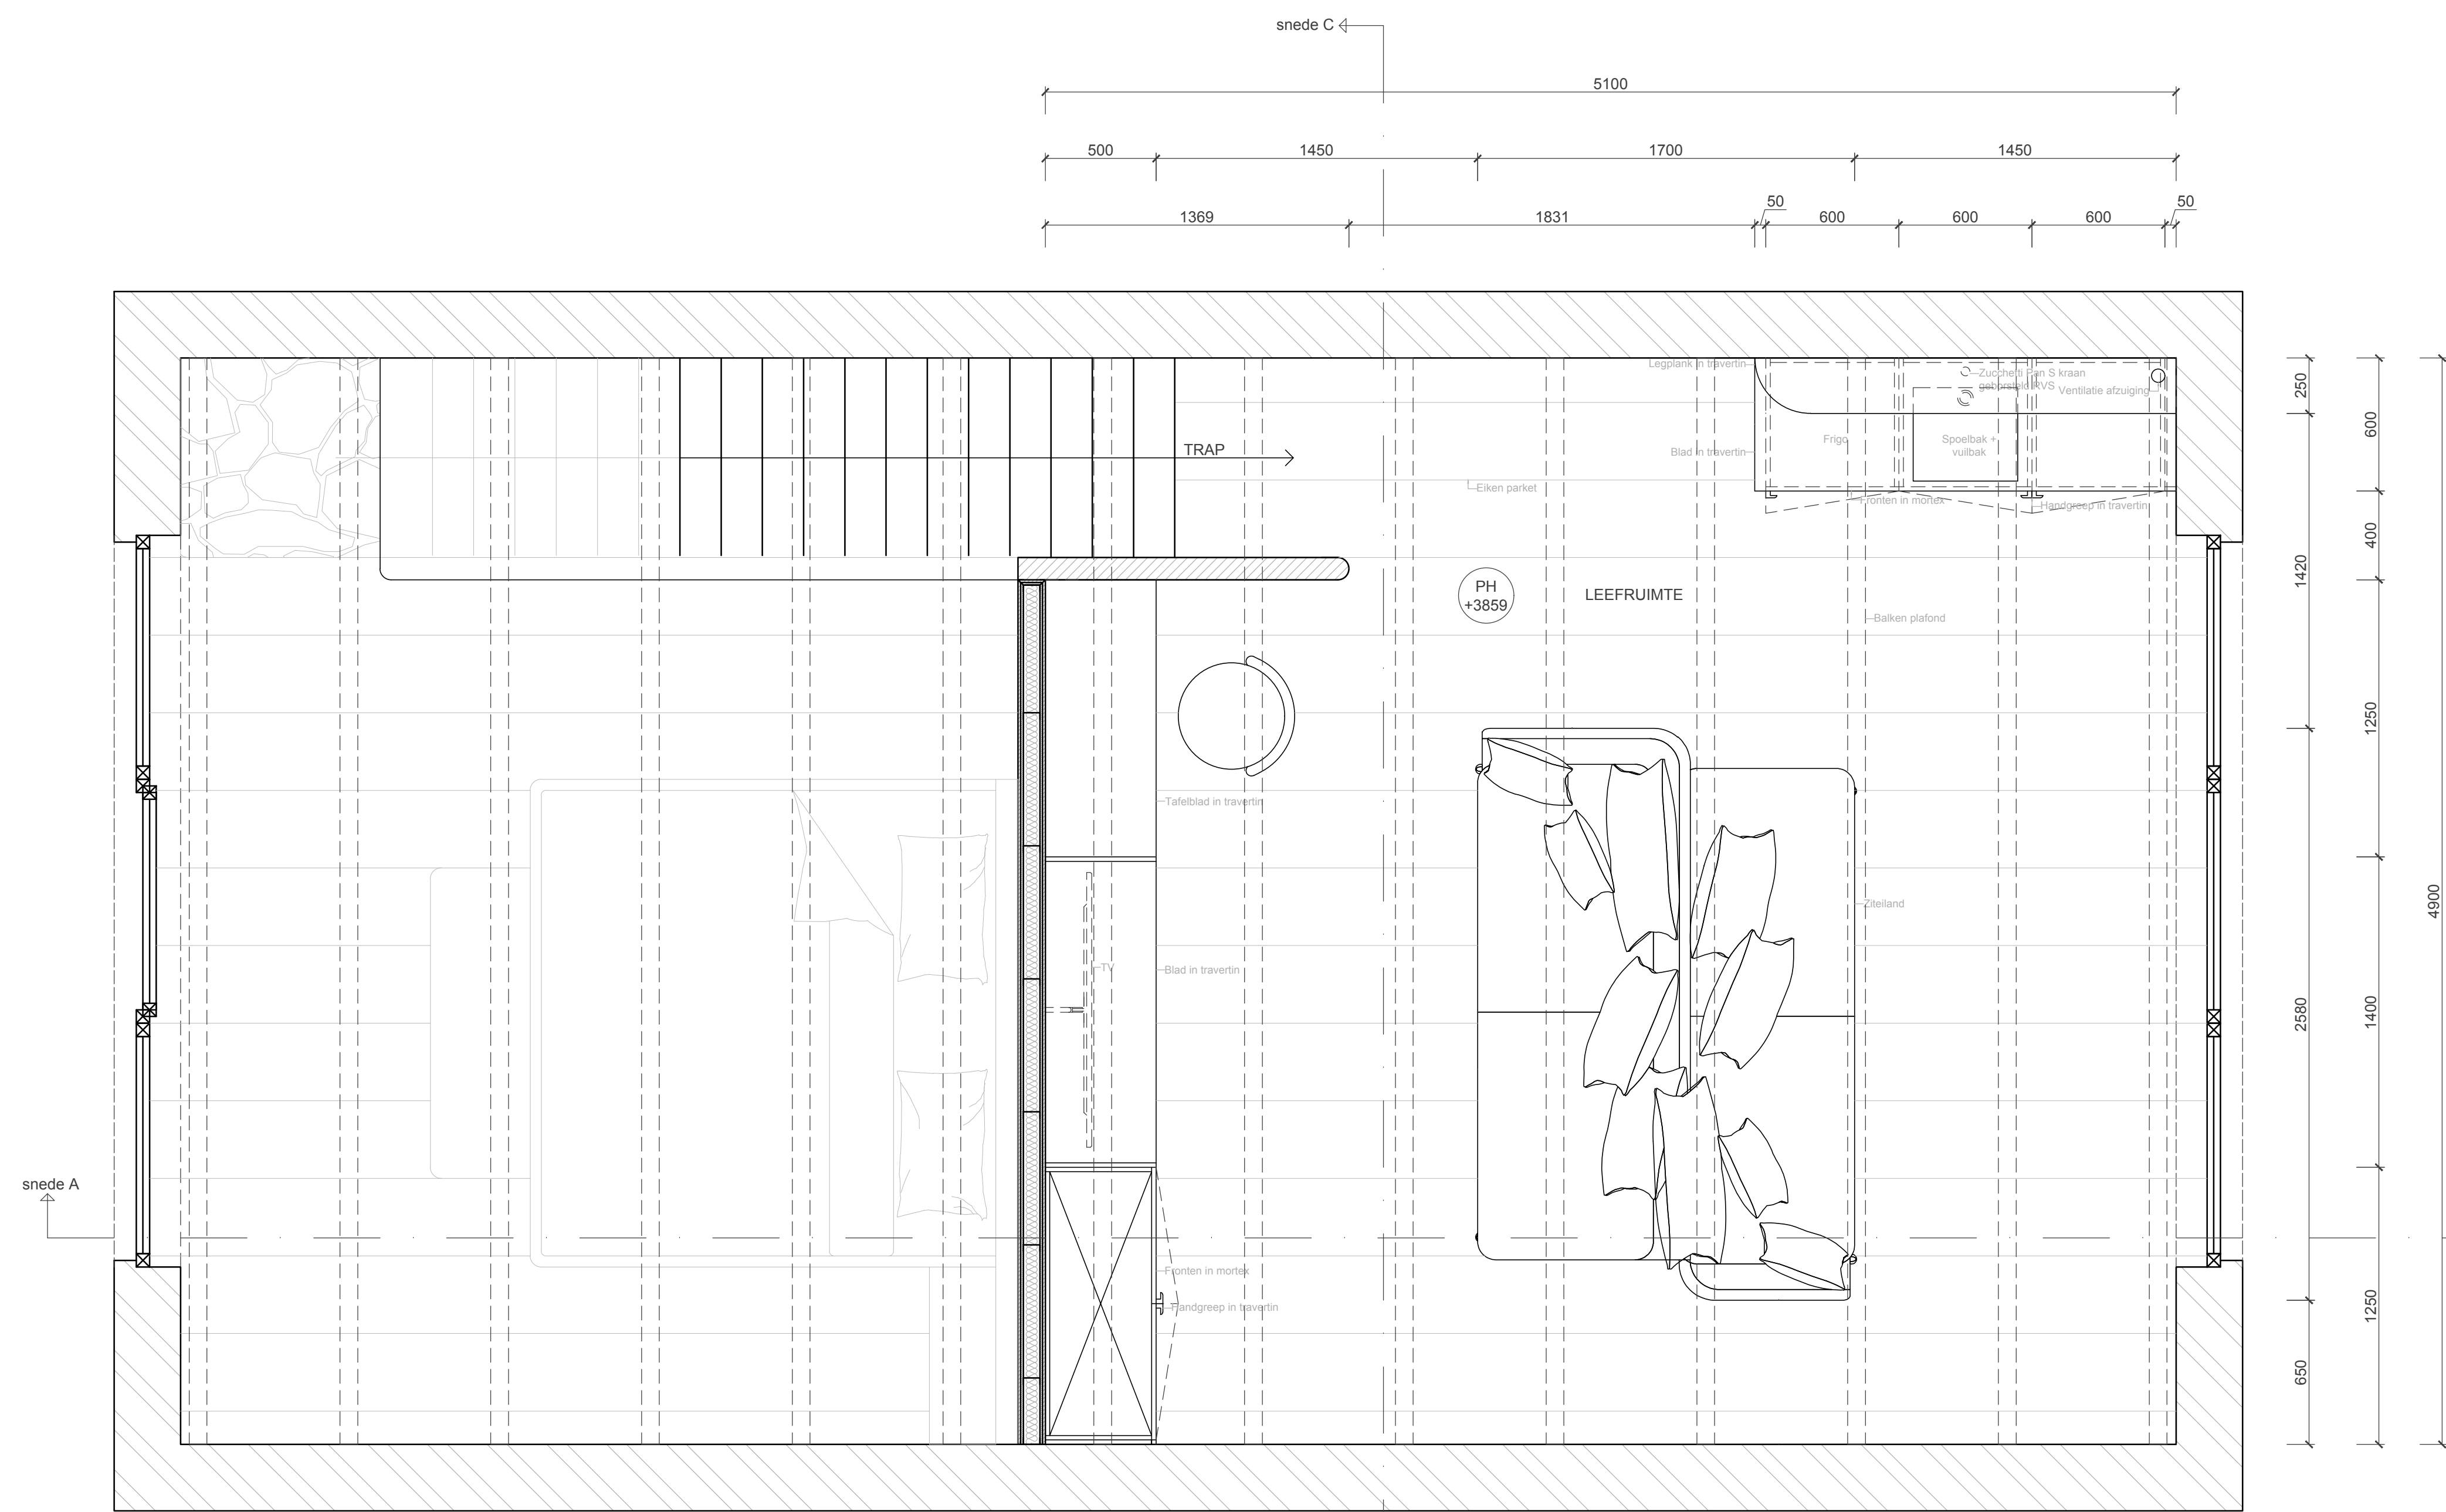


PLATTEGROND EERSTE VERDIEP 1:20

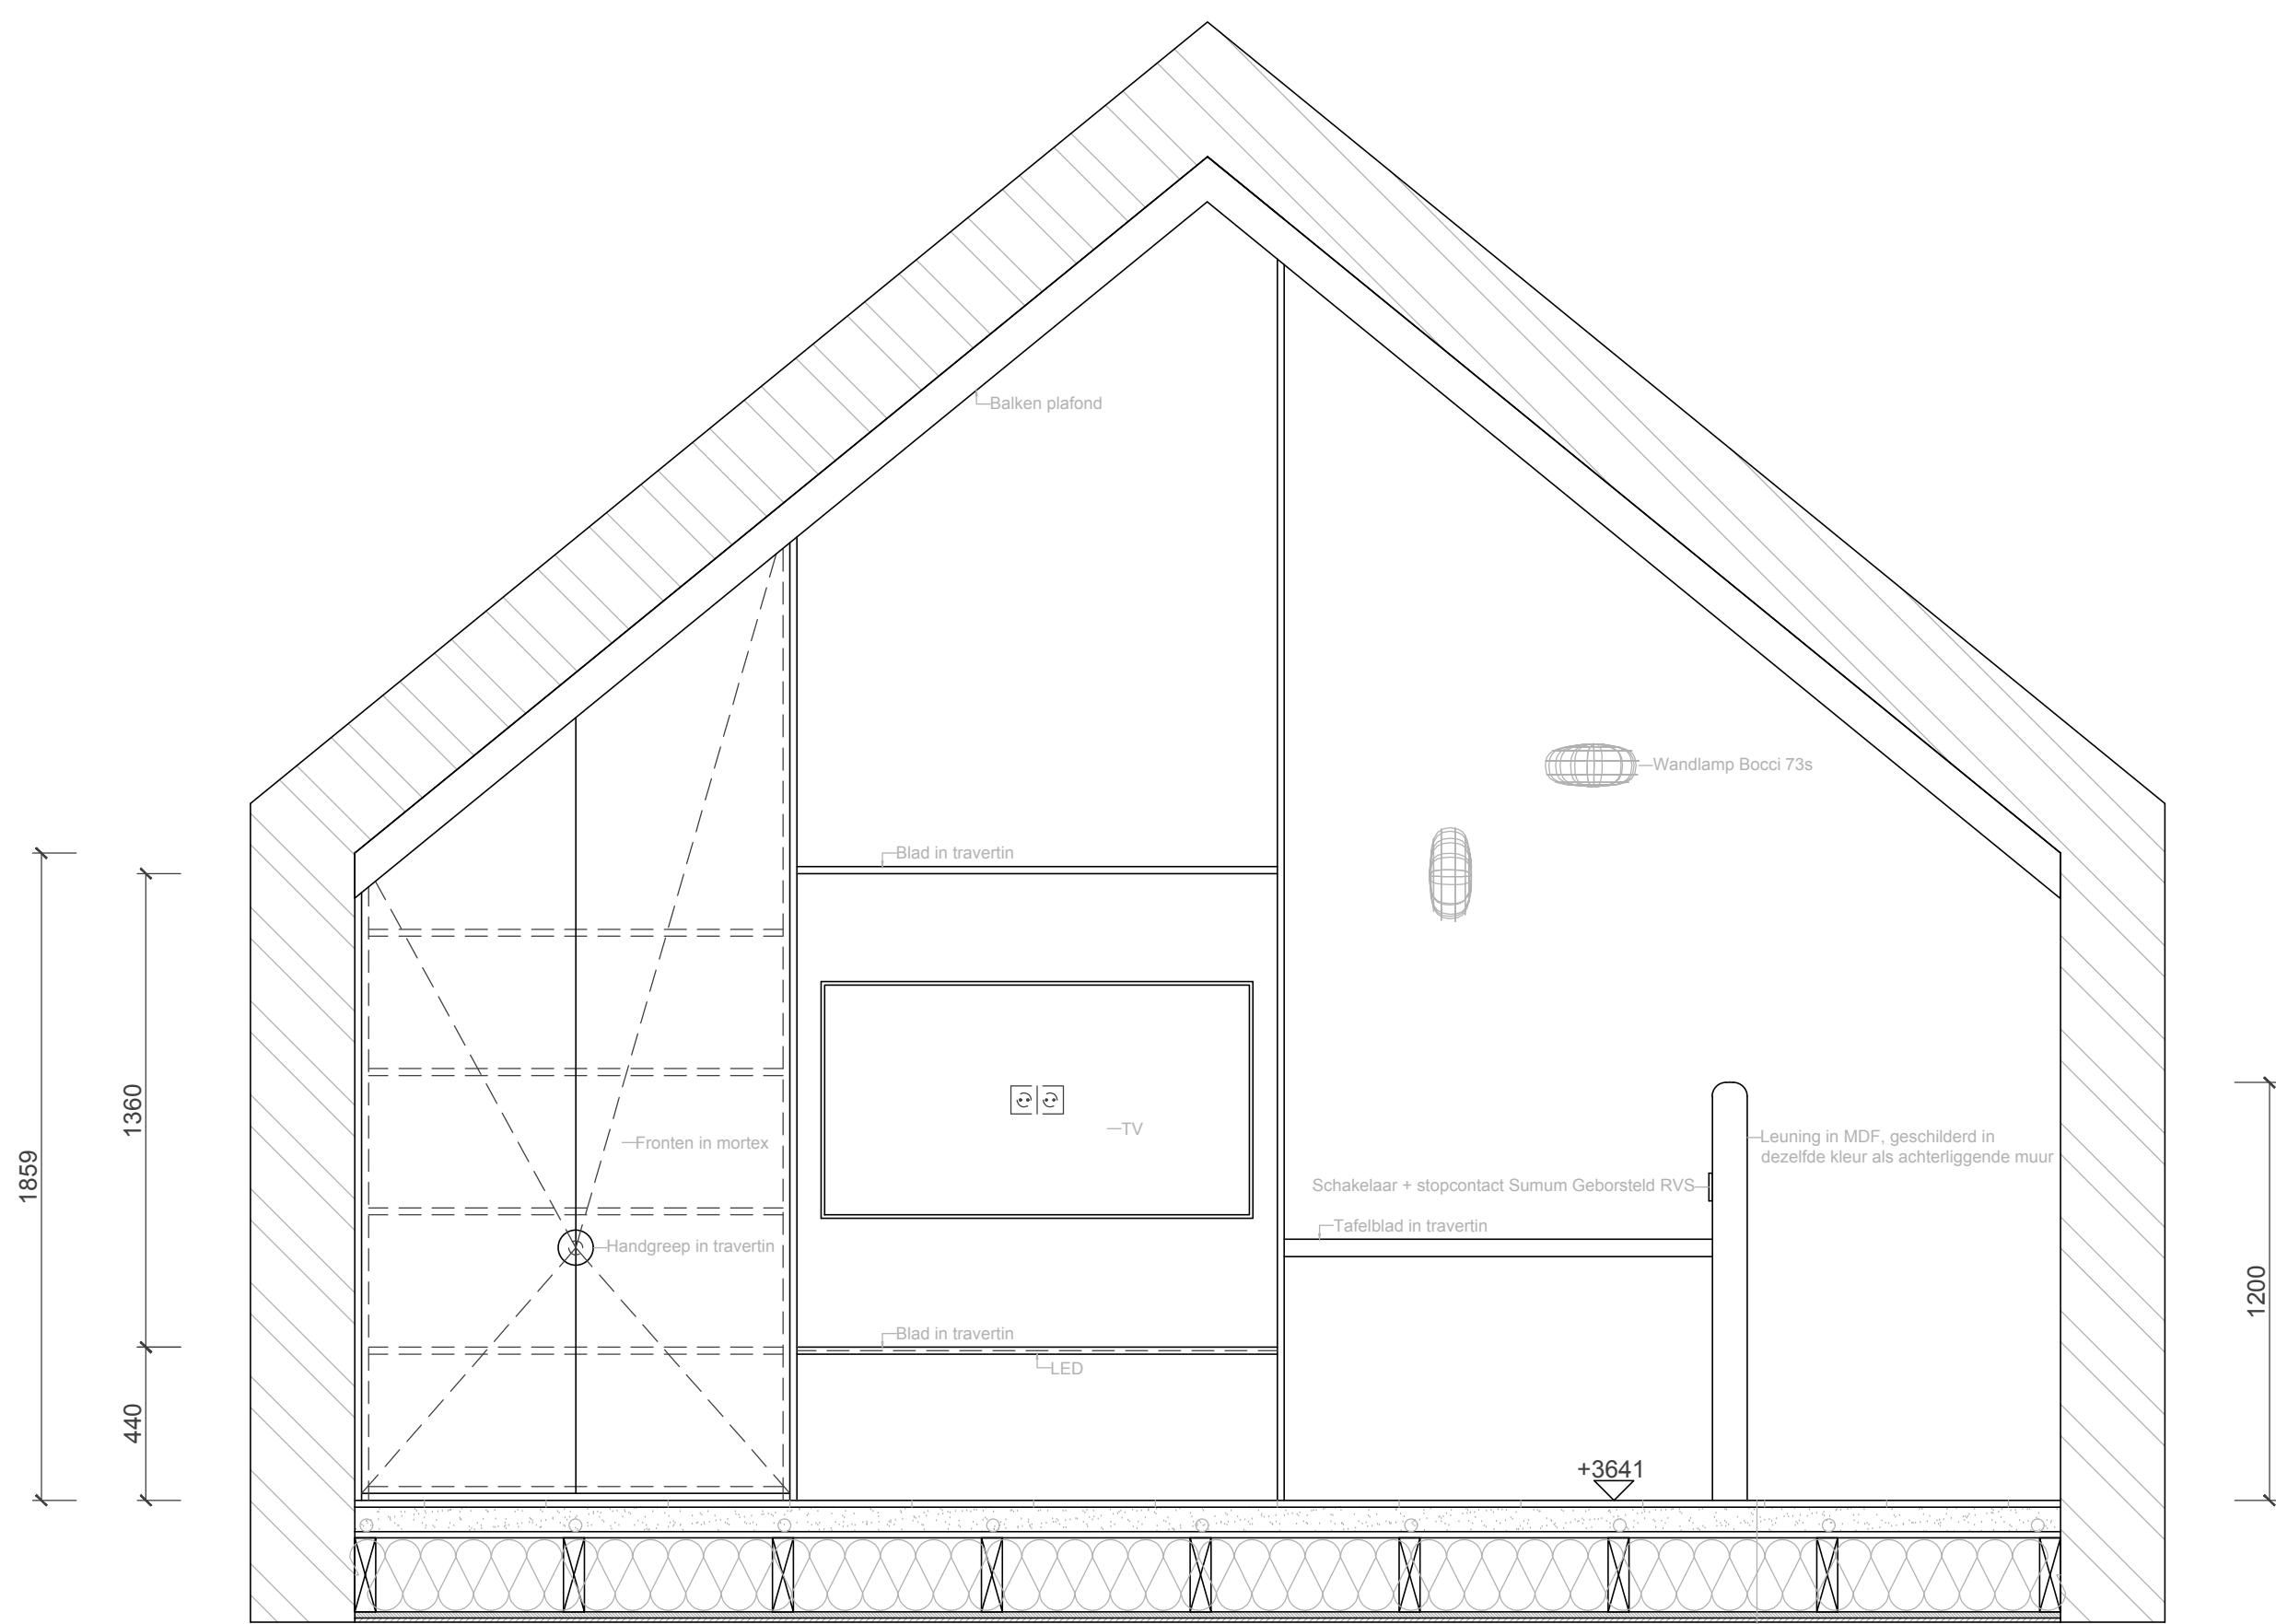


SNEDE CC' 1:20

- Vloerverwarming parket 20 mm
- Chape + vloerverwarming 70 mm
- Fermacell 18 mm
- Houten roosterling + isolatie 212 mm
- OSB 18 mm
- Gyproc 12 mm

- Butermuur
- Wand
- Gyproc
- OSB
- Vloerverwarming
- Isolatie
- Chape
- Beton

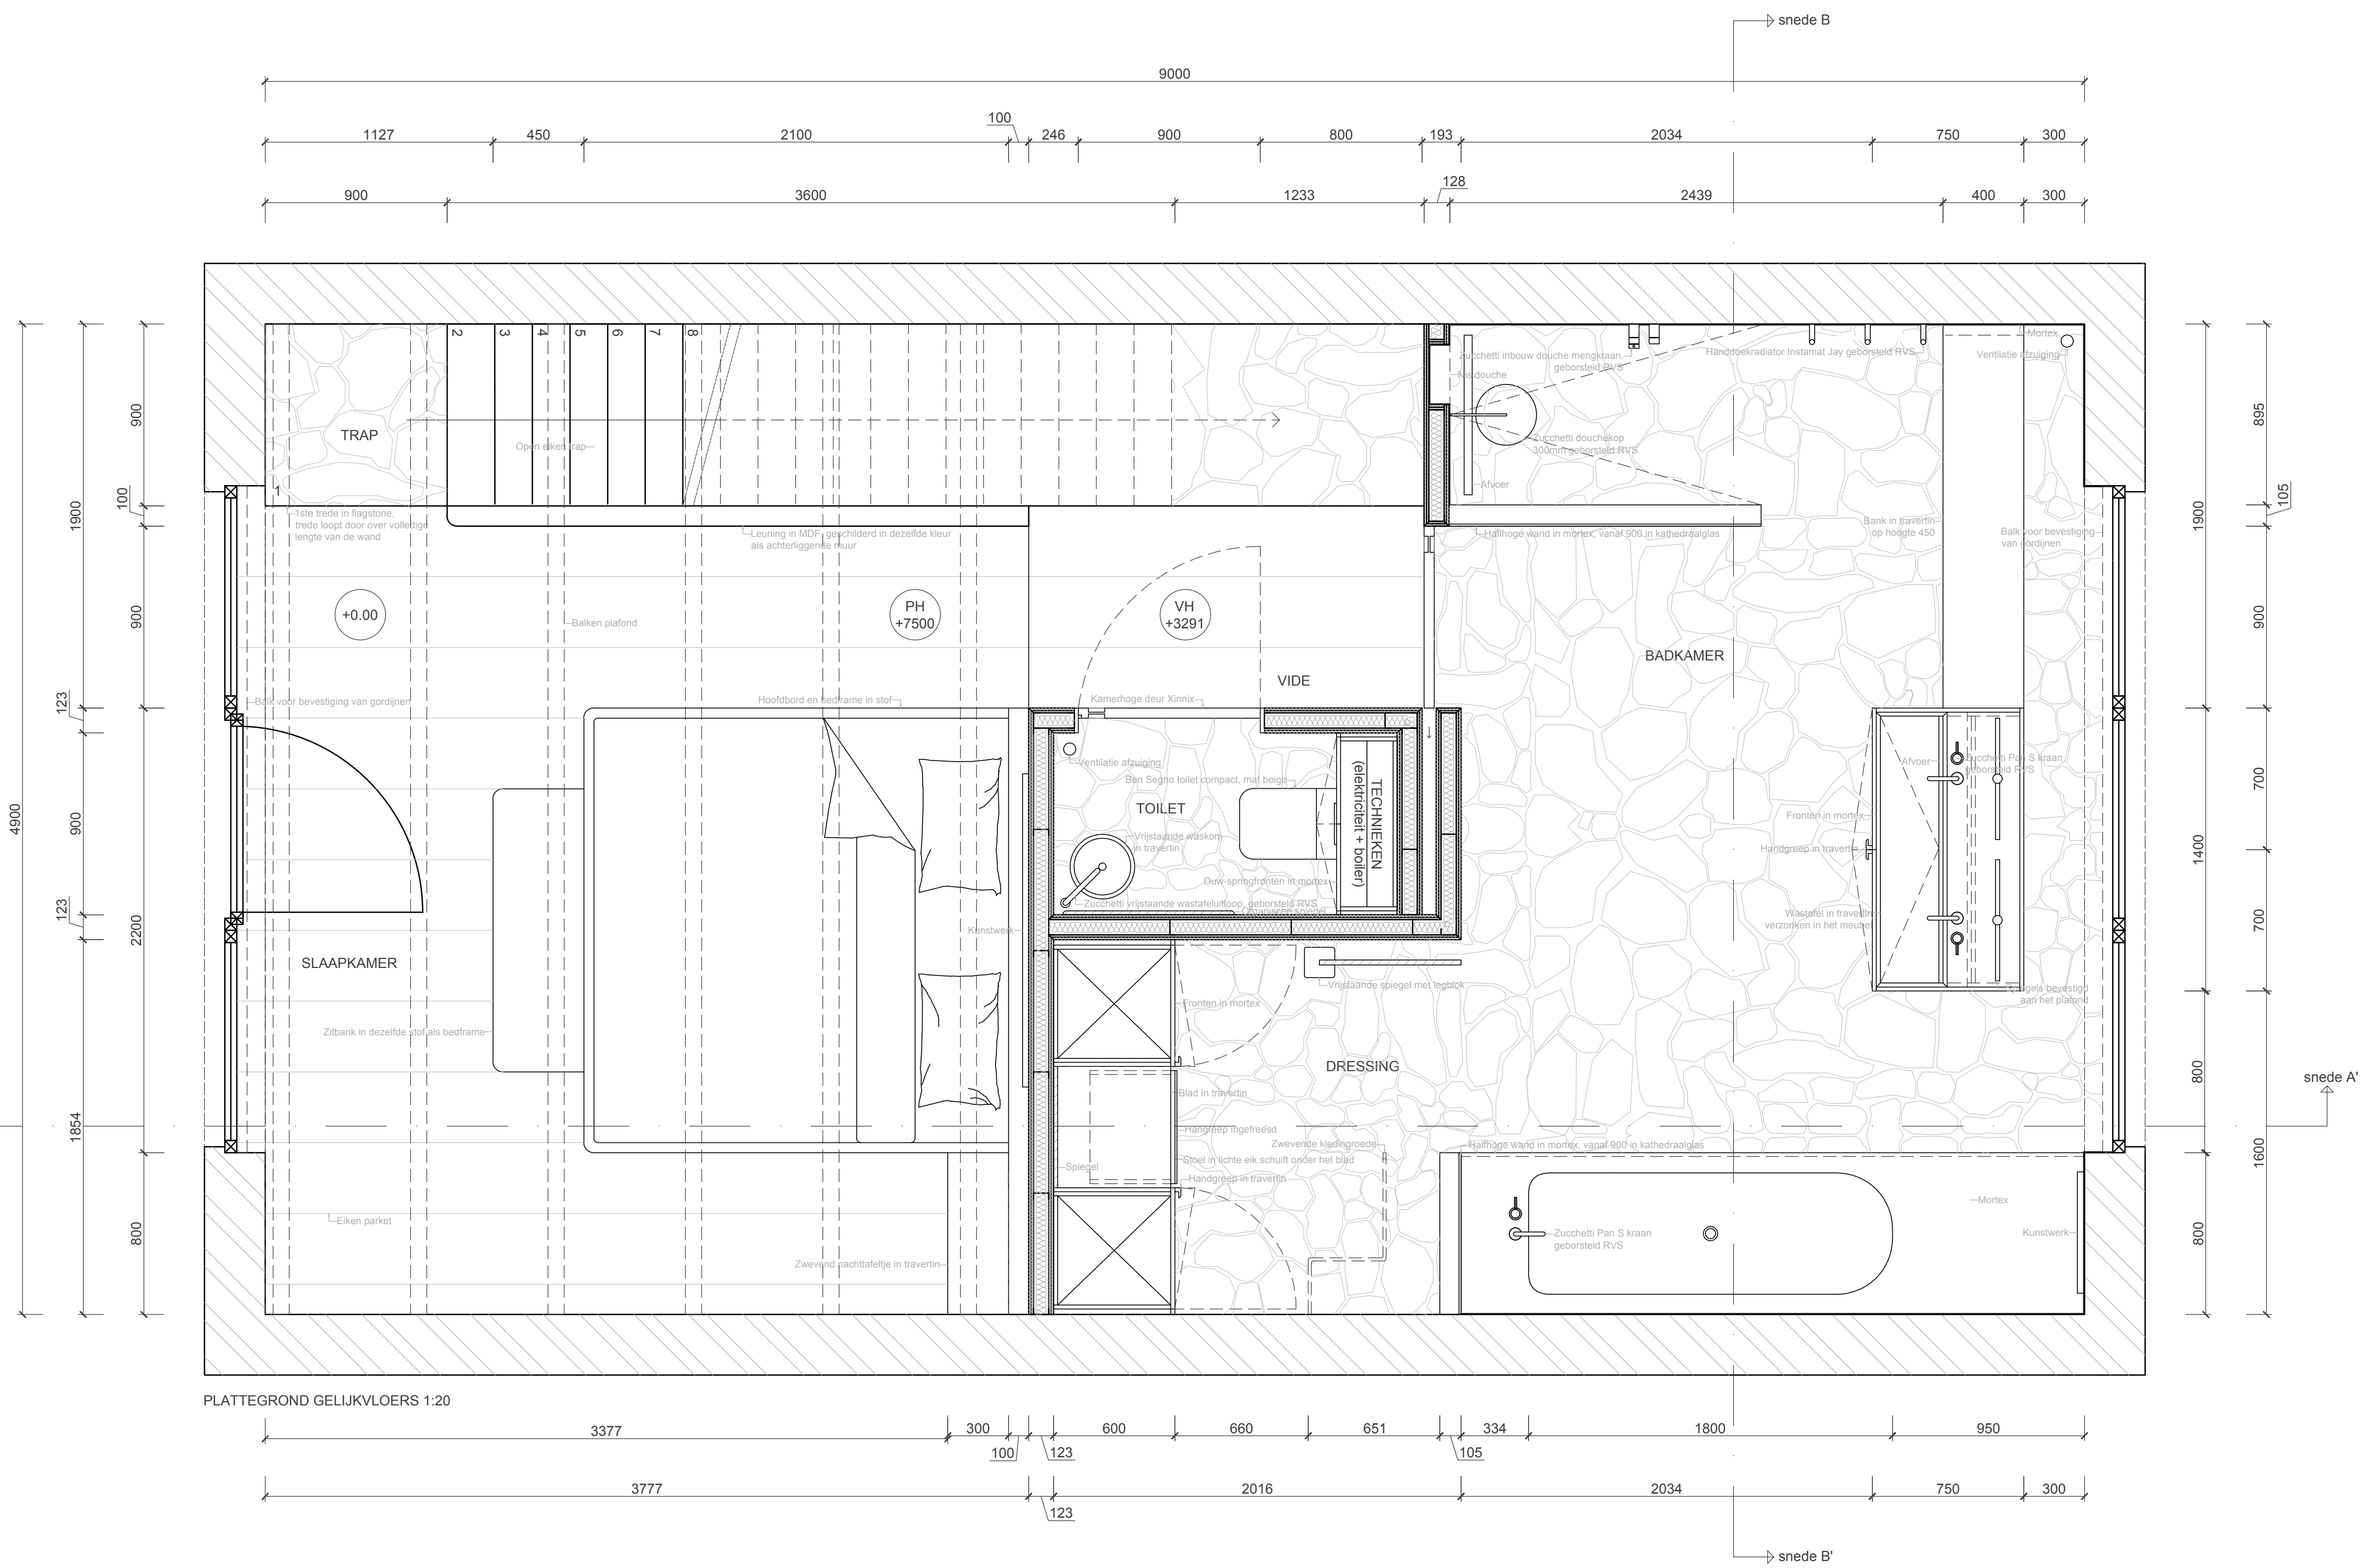

PLATTEGROND GELIJKVLOERS 1:20

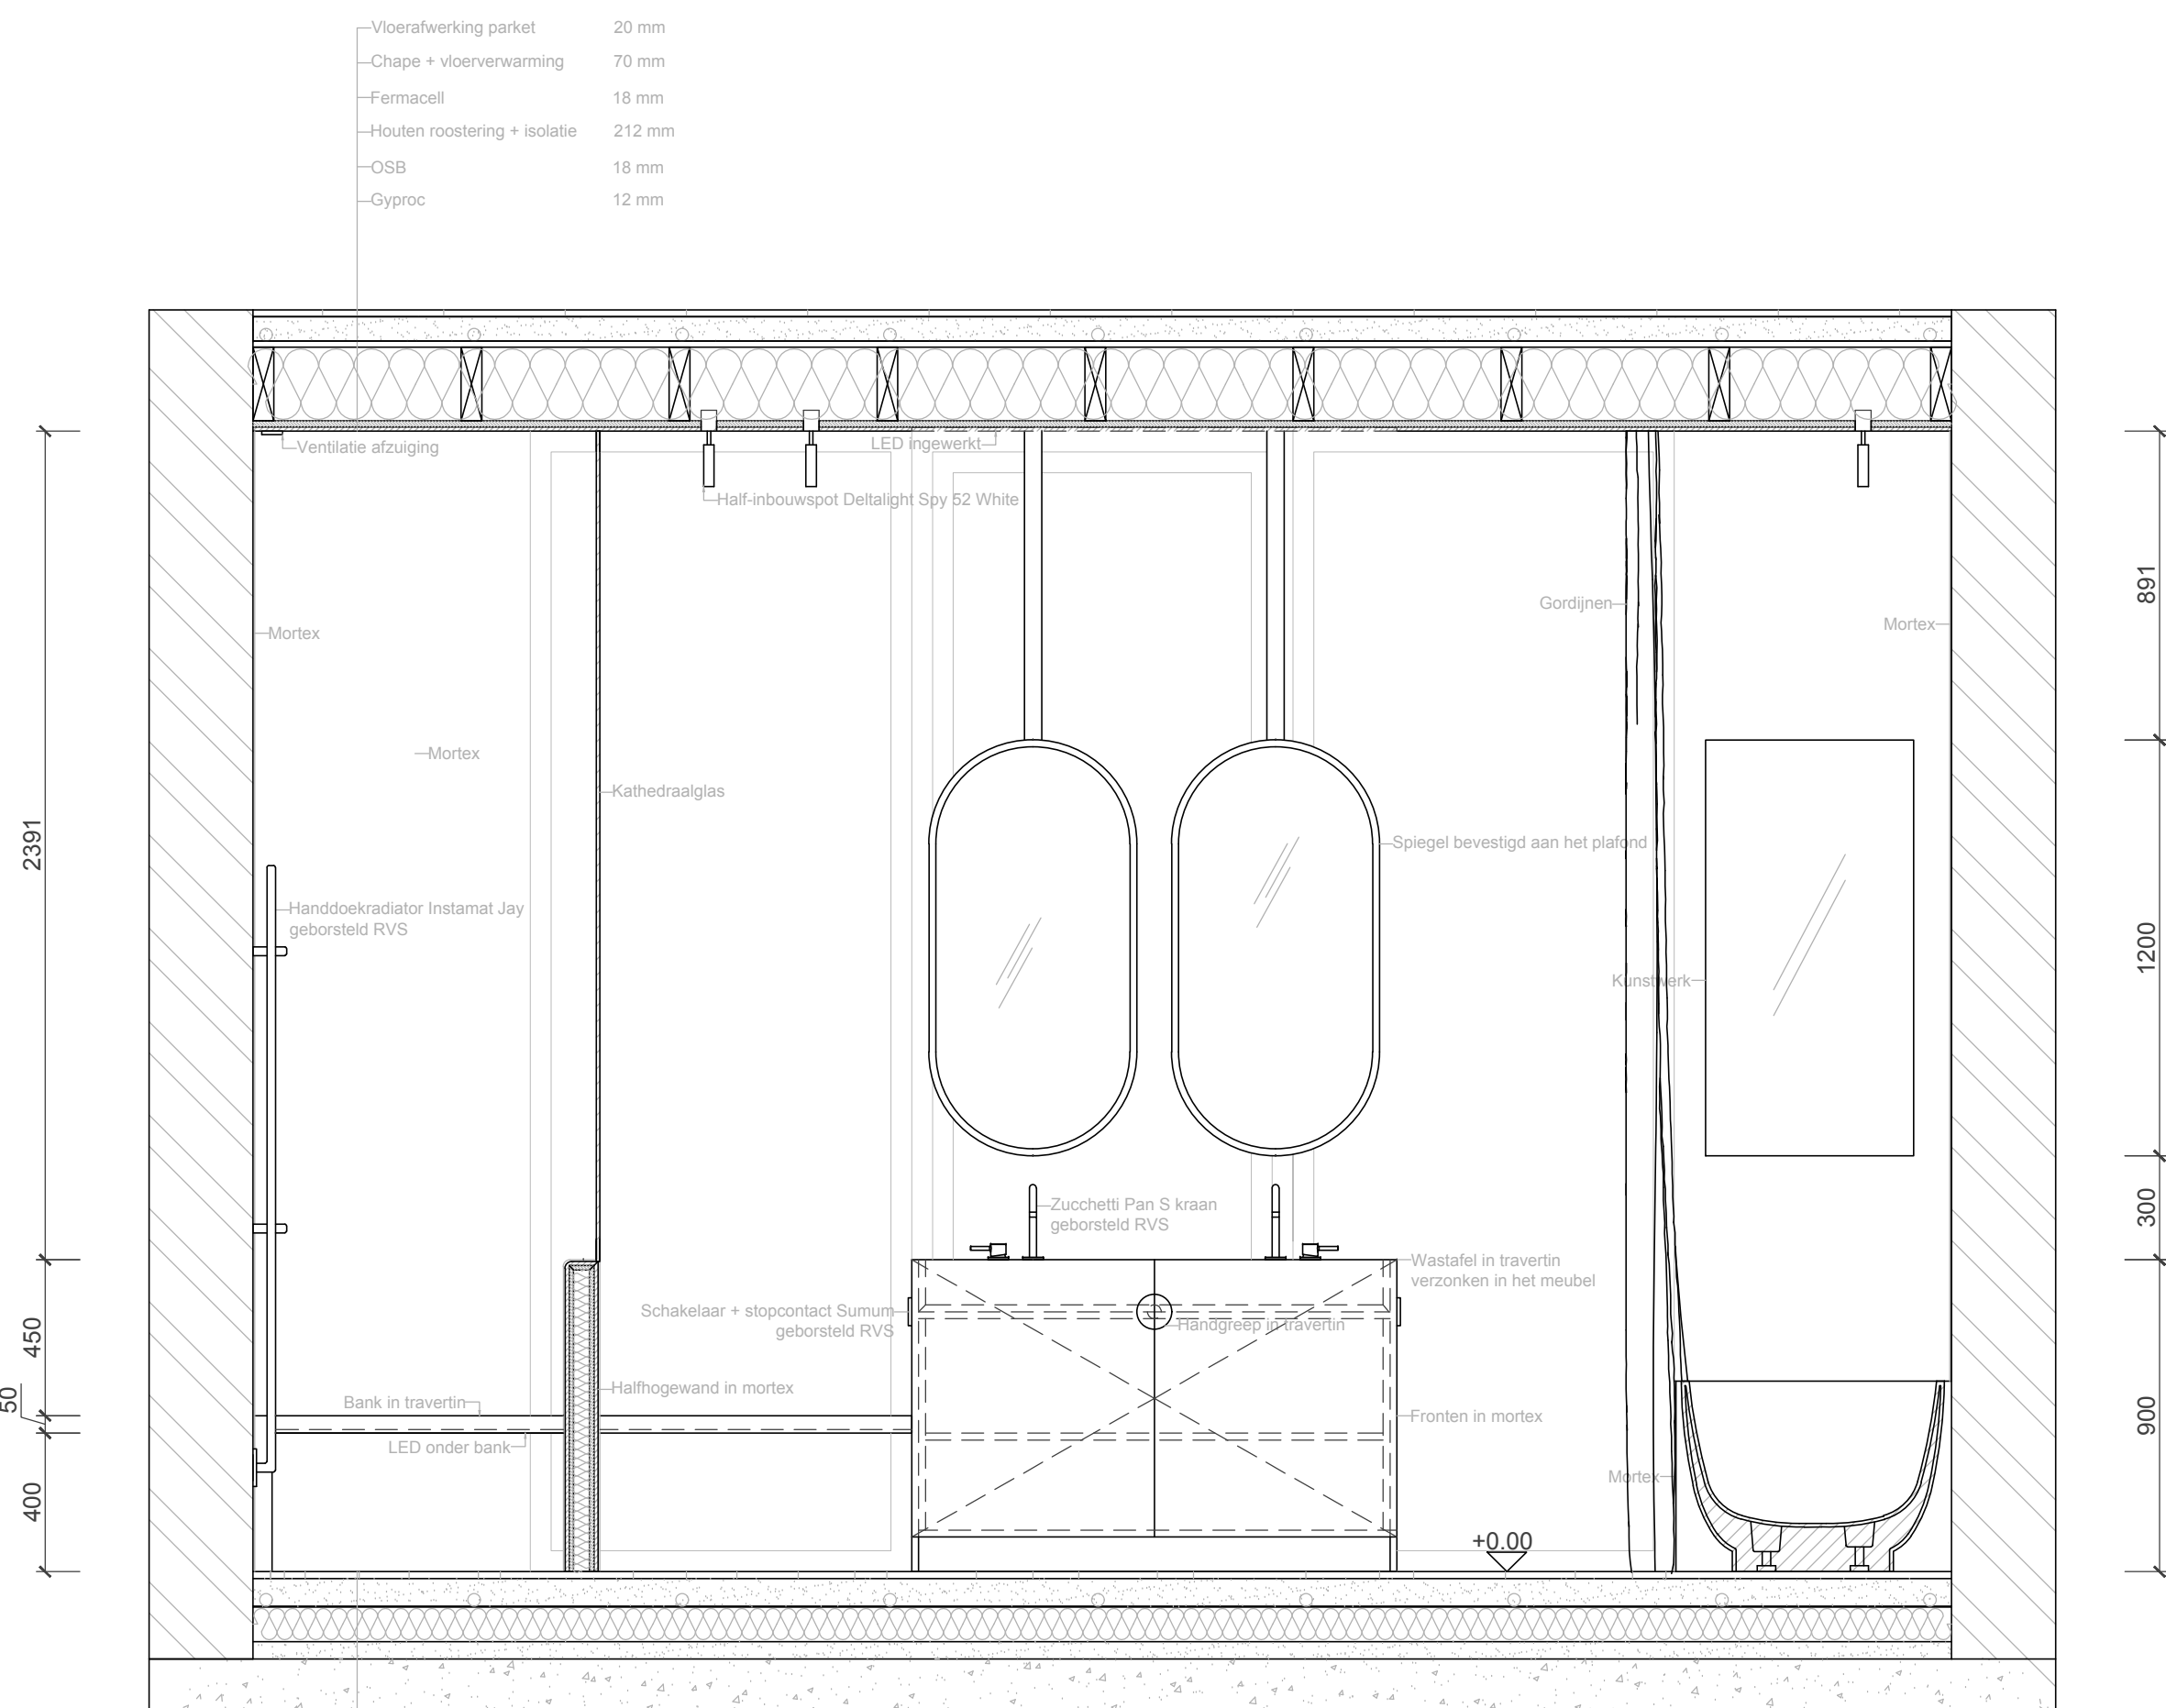

- Vloerverwarming parket 20 mm
- Chape + vloerverwarming 70 mm
- Fermacell 18 mm
- Houten roosterling + isolatie 212 mm
- OSB 18 mm
- Gyproc 12 mm

ANN-SOPHIE
VERSCHUERE

PROJECT : Ontwerp 2de verblijf
KLANT : Tiny House
ADRES : Ardennen

ONTWERPER : Ann-Sophie Verschuere
DATUM : 10 februari 2026
SCHAAL : 1:20
AANTAL BLADZIJDEN : 3

Architectural floor plan of a two-story building. The plan shows a central corridor (L-Spiegel) flanked by two large rooms. The overall dimensions are 1854 in width and 800 in depth. The plan includes various annotations for materials and construction details, such as "LED in detail", "Blad in travers", "Handgreep ingebouwd", "Blad in frame als schuif onder het tijg", "L-Spiegel", "LED in detail", "Corpus in aluminium met metaalcoating", and "L-Spiegel". The plan is labeled "PLATTEGROND 1:10" and includes section lines "sne D" and "sne E".

Technical drawing of a wall-mounted cabinet. The overall height is 2480 mm and the overall width is 3390 mm. The cabinet features a large main compartment and a smaller lower compartment. Labels include: "LED in plafond" (LED in ceiling), "Vast paneel" (Fixed panel), "Kastdeur geopend" (Cabinet door open), "Fijnt in MDF met moes" (Fine in MDF with moose), "LED ingebouwd" (LED built-in), "Buitenaanzicht kast in MDF met moes" (Exterior view of cabinet in MDF with moose), "Legsteek" (Leg piece), "Blaas in steen" (Blow in stone), and "←" (Arrow pointing left).


[illegible]

The diagram illustrates a cross-section of a wall with the following layers from top to bottom:


- Buitenmuur**: The outermost layer, shown with diagonal hatching.
- Wand**: The main wall structure, shown with horizontal hatching.
- Gypoc**: A layer of plaster, shown with a stippled pattern.
- OSB**: A layer of oriented strand board, shown with a solid grey fill.
- Vloerverwarming**: A heating system, represented by two small circles.
- Isolatie**: An insulation layer, shown with a wavy, zigzag pattern.
- Chape**: A concrete screed layer, shown with a solid grey fill.
- Beton**: The base concrete slab, shown with a solid grey fill.




ONTWERPER :	Ann-Sophie Verschuere
DATUM :	10 februari 2026
SCHAAL :	1:10 (meubel) 1:20 (sneede)
AANTAL BLADZIJDEN :	3

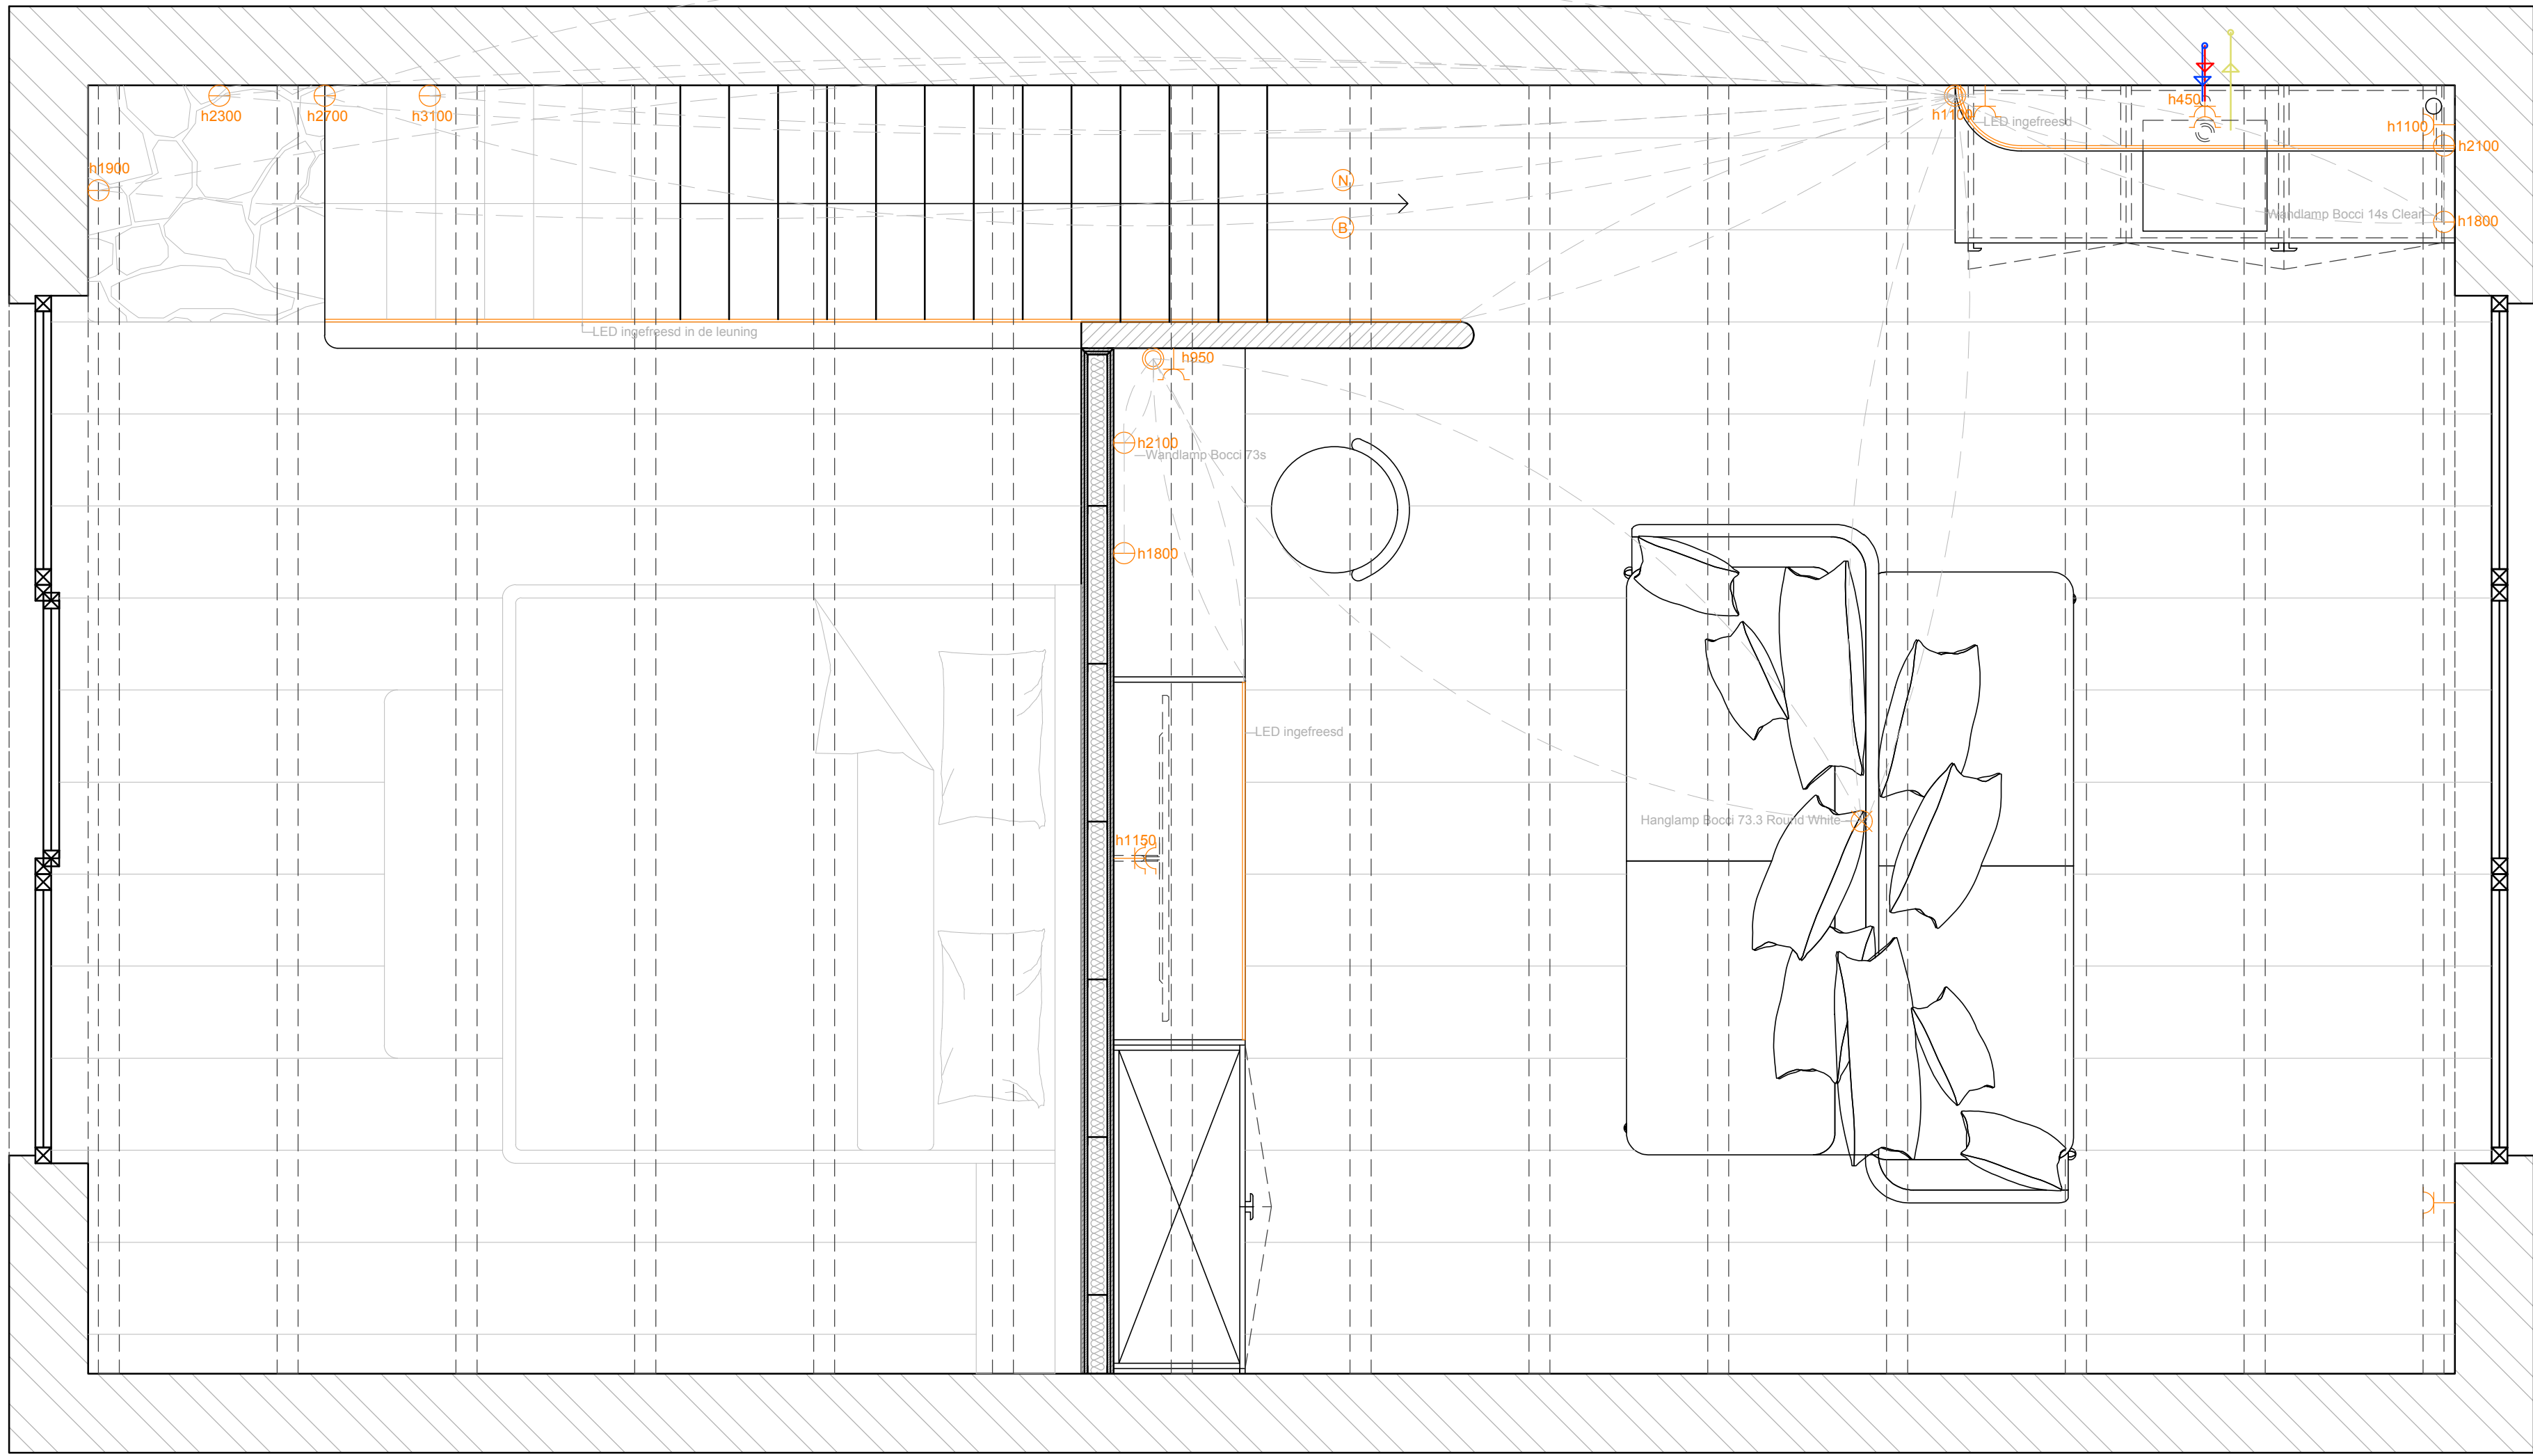

TECHNISCH PLAN EERSTE VERDIEP (sanitair + elektriciteit) 1:20

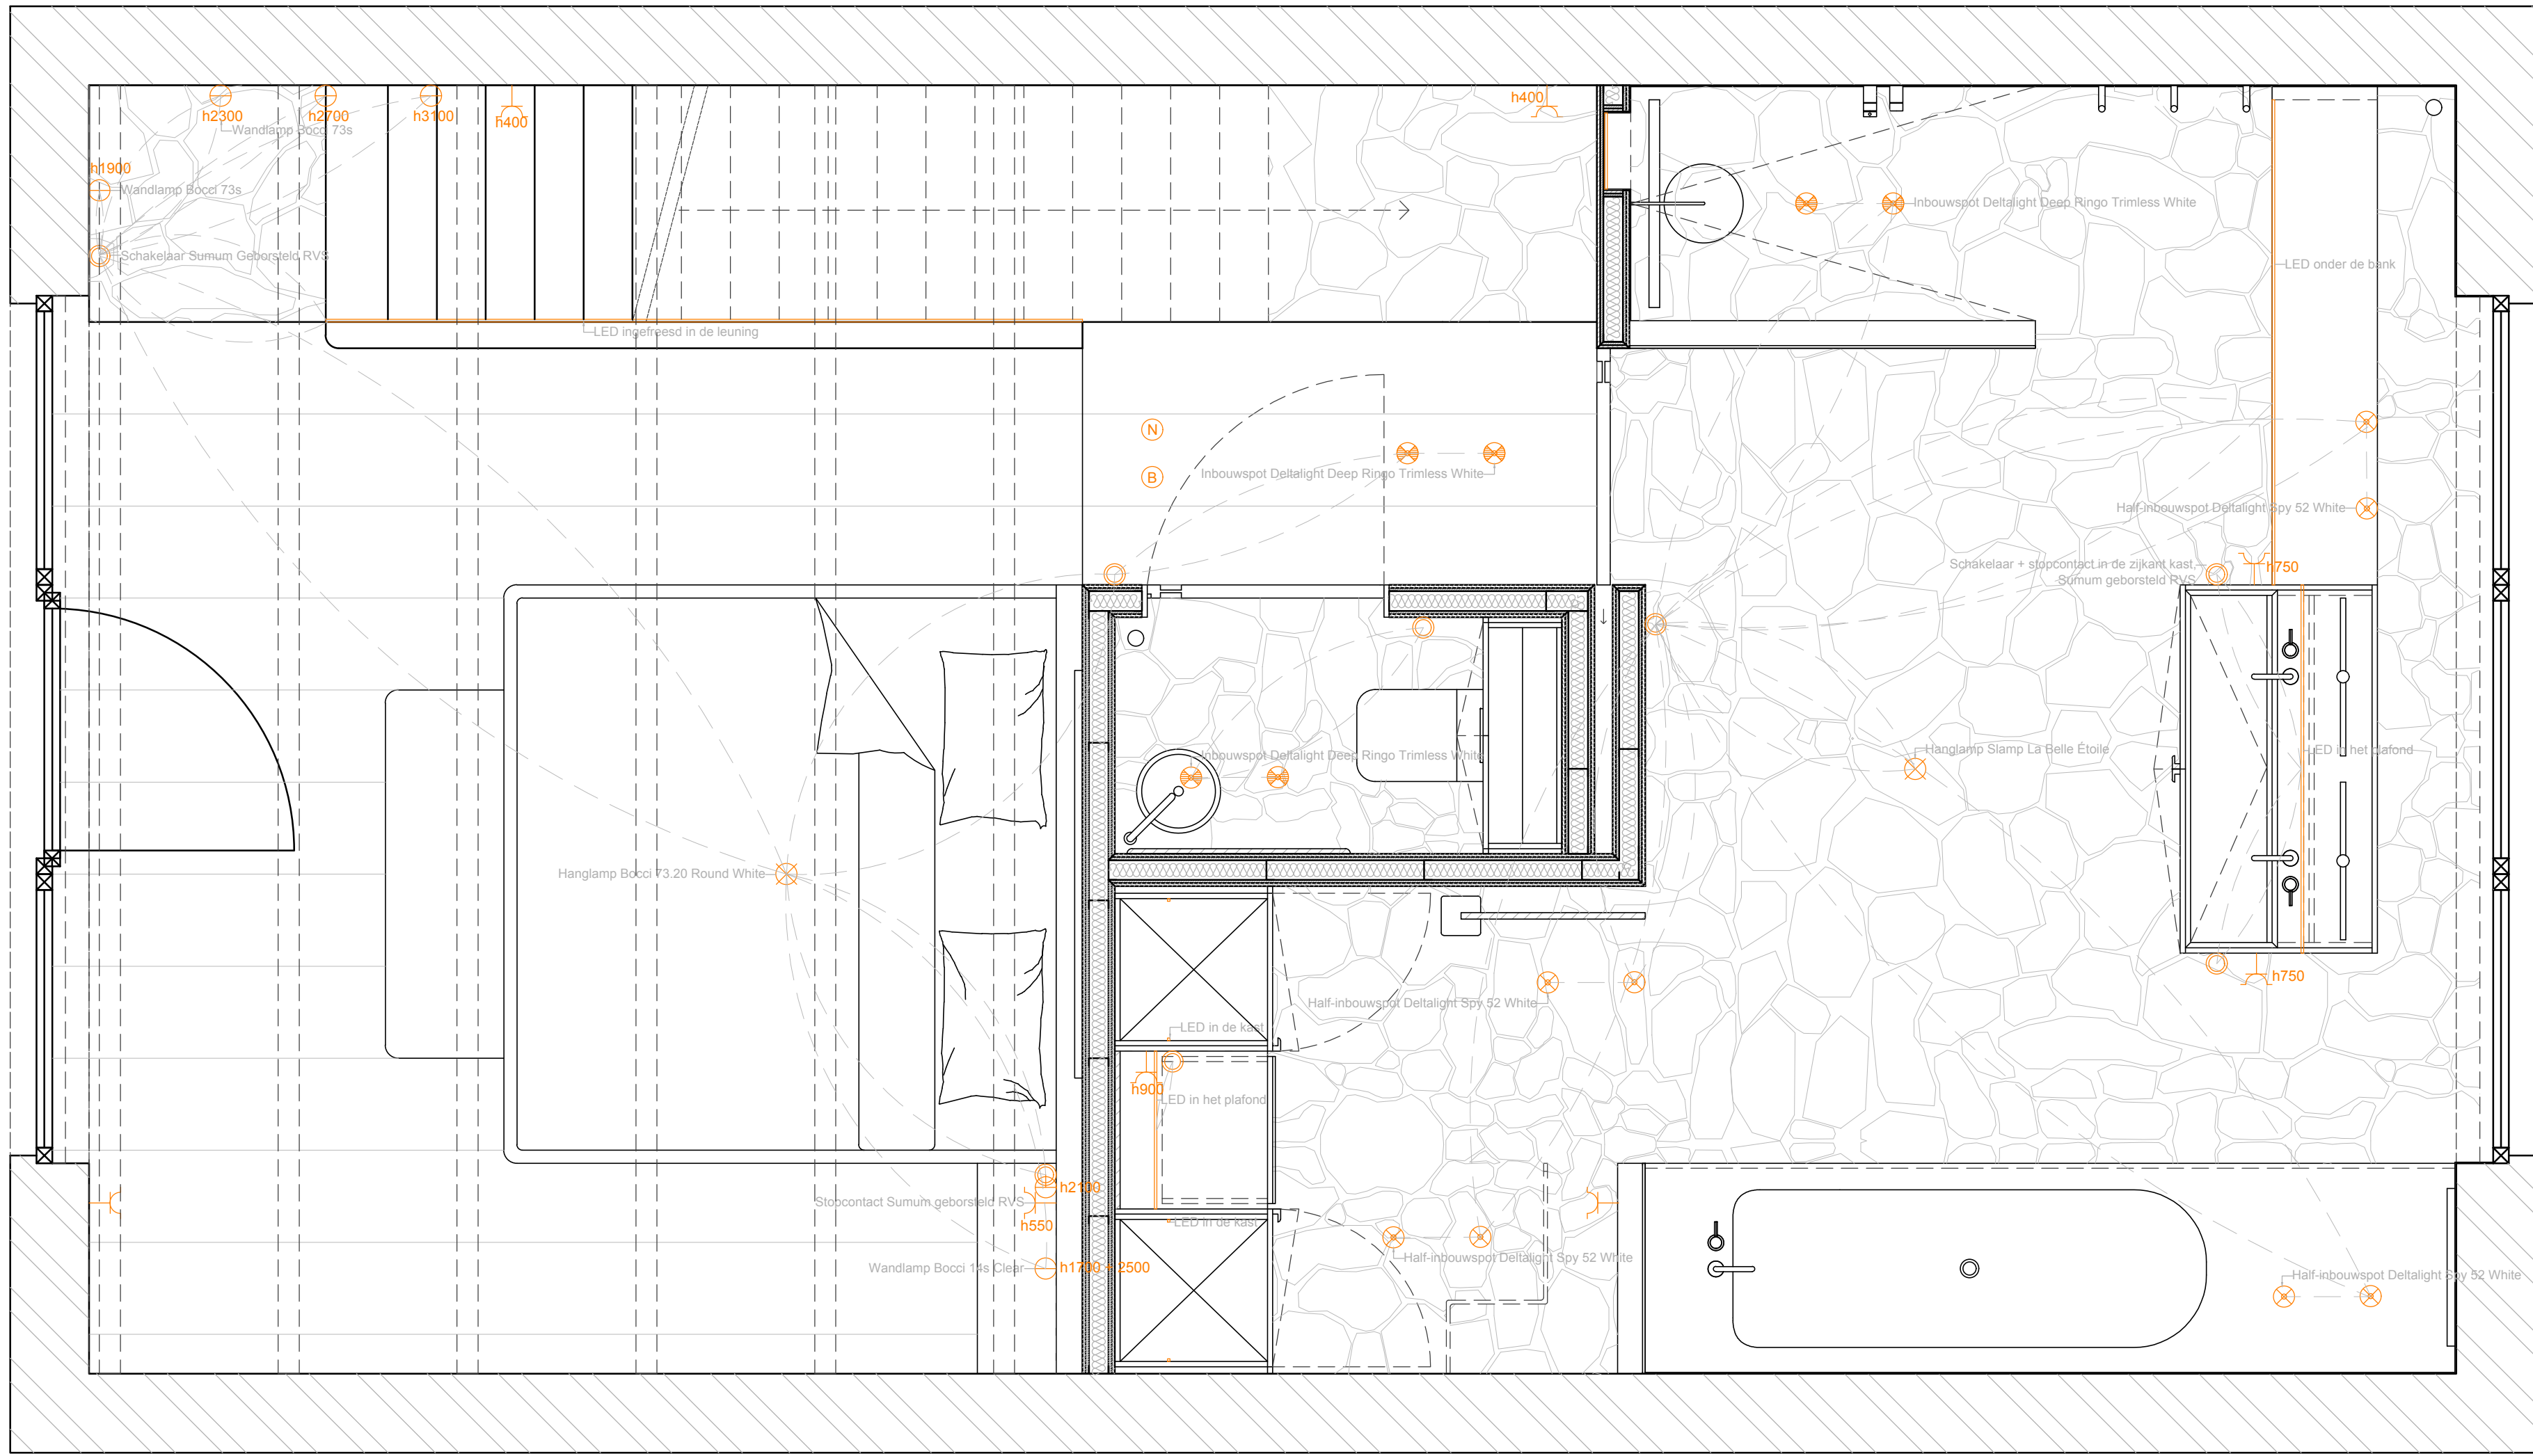

TECHNISCH PLAN GELUKVLOERS (elektriciteit) 1:20

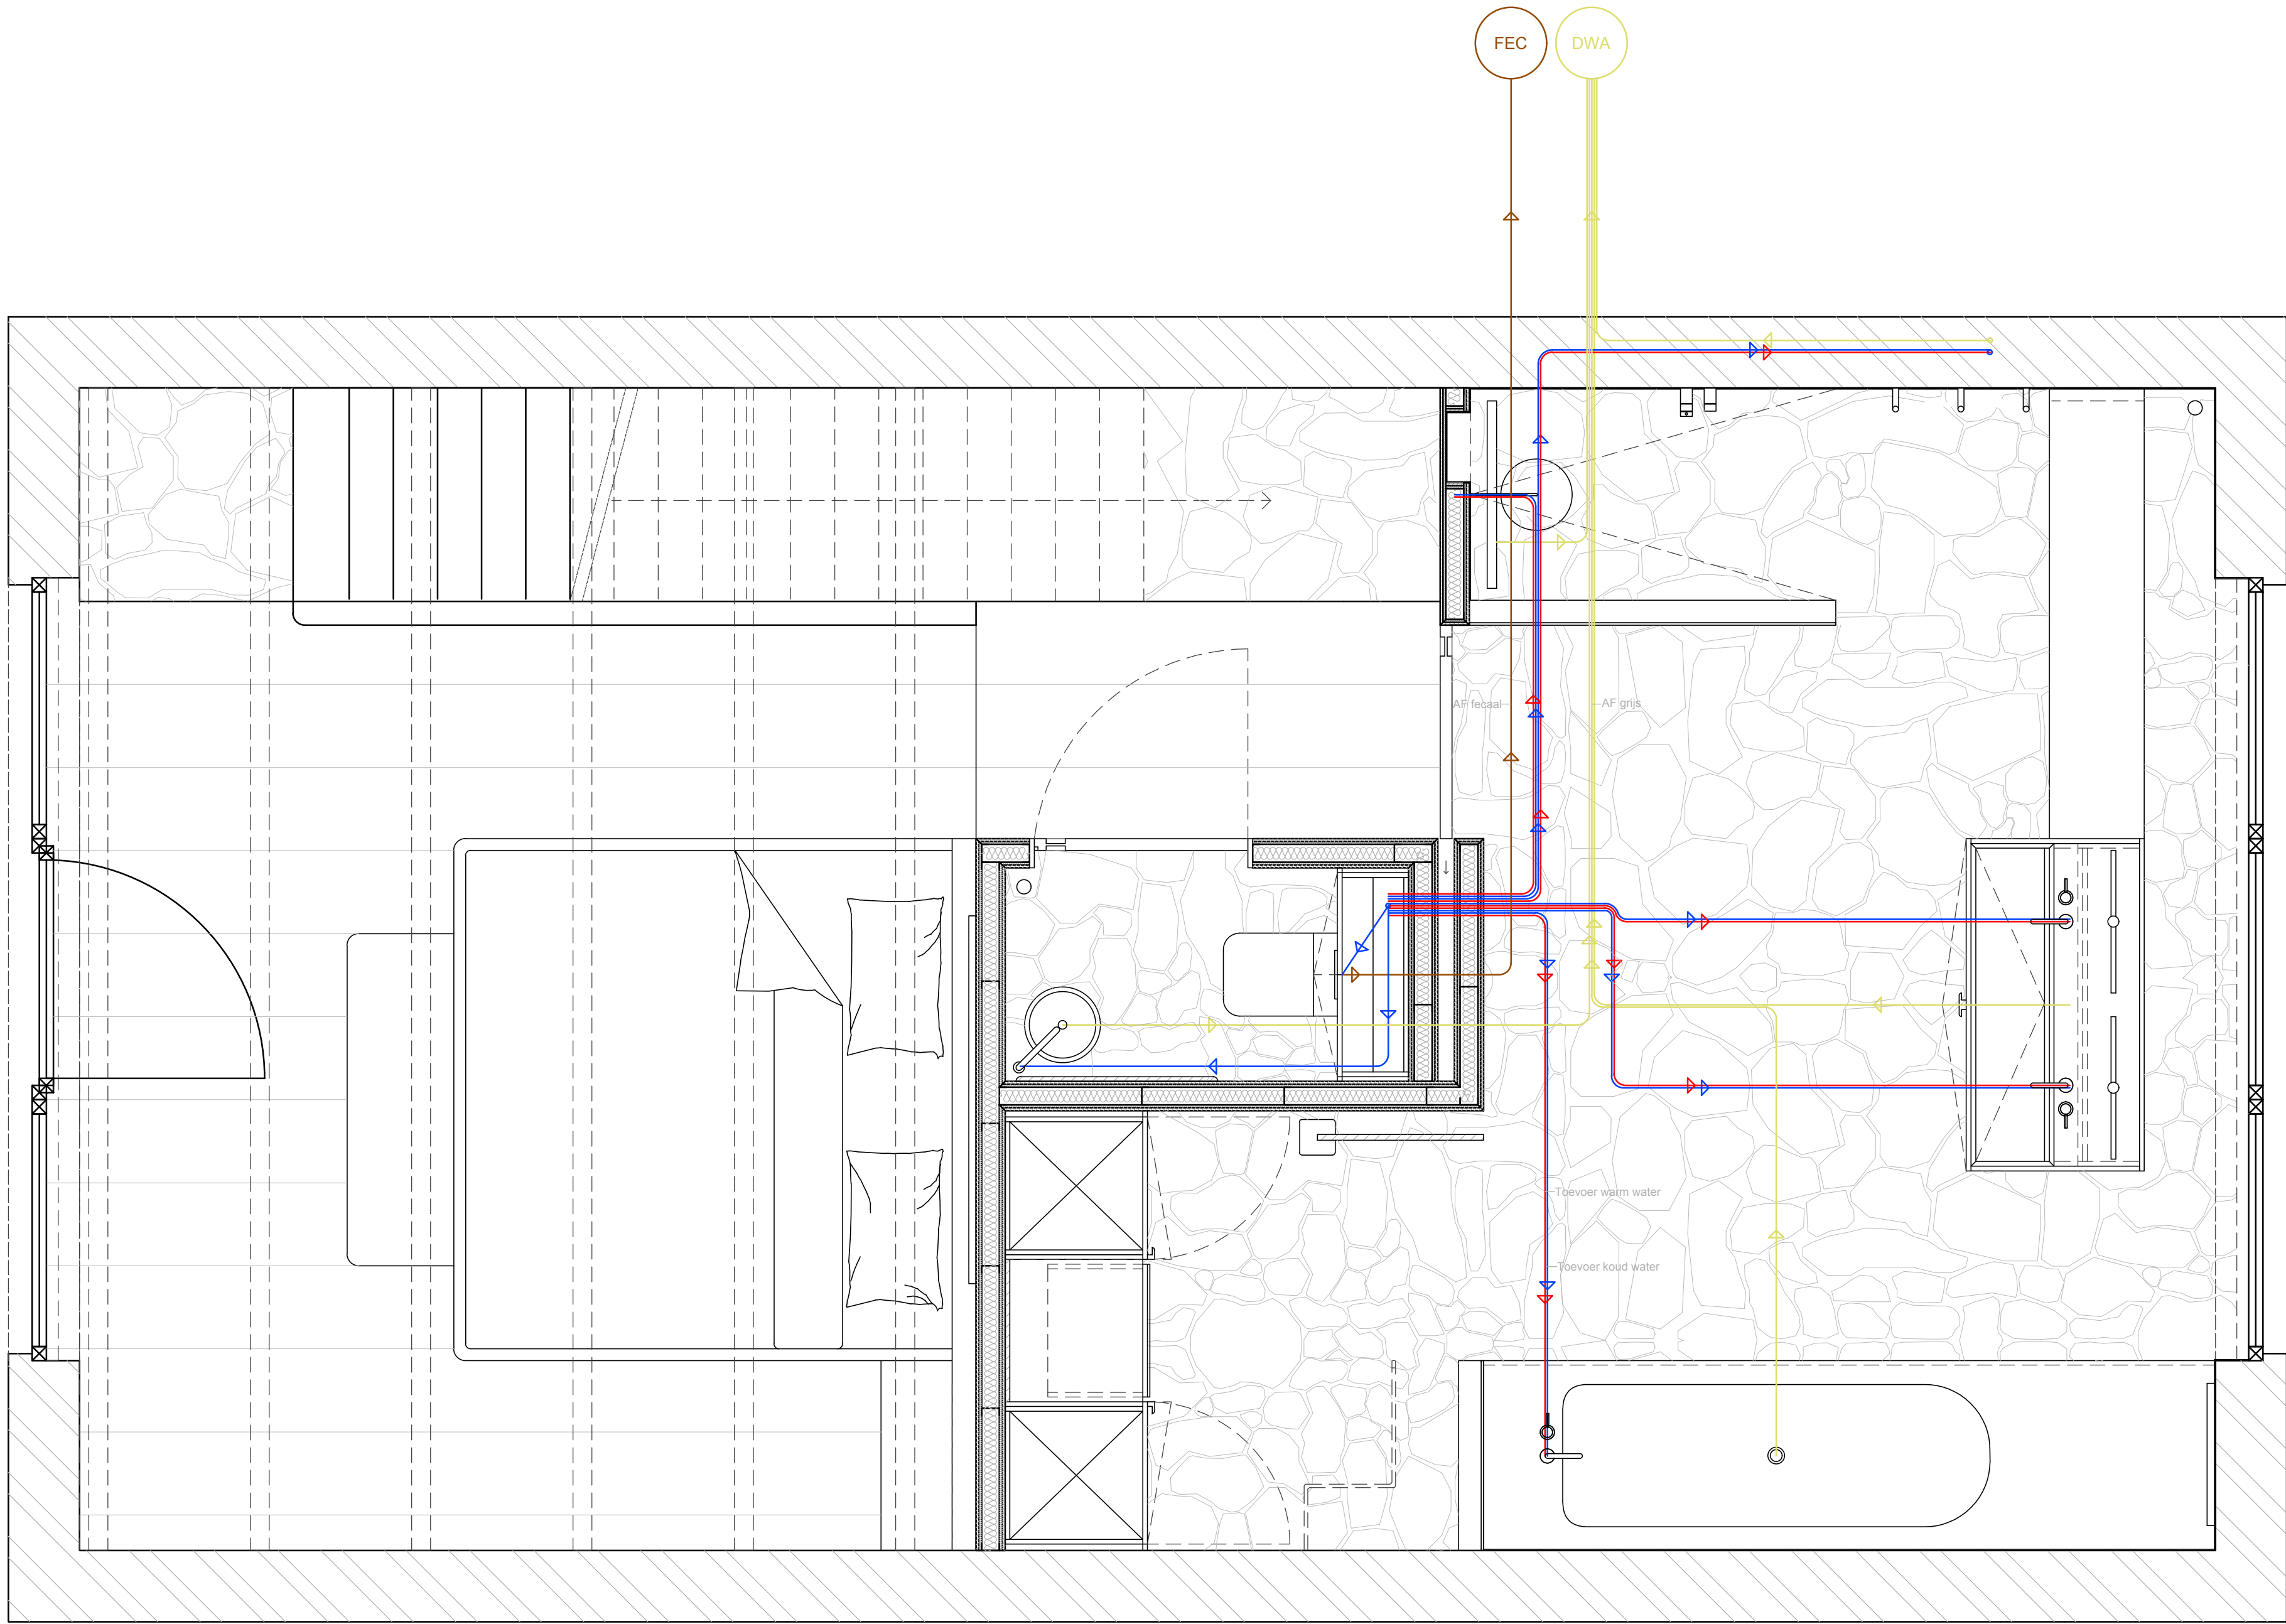

TECHNISCH PLAN GELUKVLOERS (sanitair) 1:20

- | | | | |
|--|----------------------------|--|--|
| | Buitemuur | | Wandlamp |
| | Wand | | Inbouwspot |
| | Gyproc | | Half-inbouwspot |
| | OSB | | Lichtpunt |
| | Vloerverwarming | | Noodverlichting |
| | Isolatie | | LED |
| | Beton | | Branddetectie |
| | Koudwater toevoer | | Drukschakelaar (standaardhoogte 1000 mm) |
| | Warmwater toevoer | | Stopcontact (standaardhoogte 250 mm) |
| | Huishoudelijk water afvoer | | Dubbel stopcontact |
| | Fecaal water afvoer | | Stopcontact op hoogte 1500 mm |
| | | | Ventilatie |



PROJECT : Ontwerp 2de verblijf
KLANT : Tiny House
ADRES : Ardennen

ONTWERPER : Ann-Sophie Verschuere
DATUM : 10 februari 2026
SCHAAL : 1:20
AANTAL BLADZIJDEN : 3